
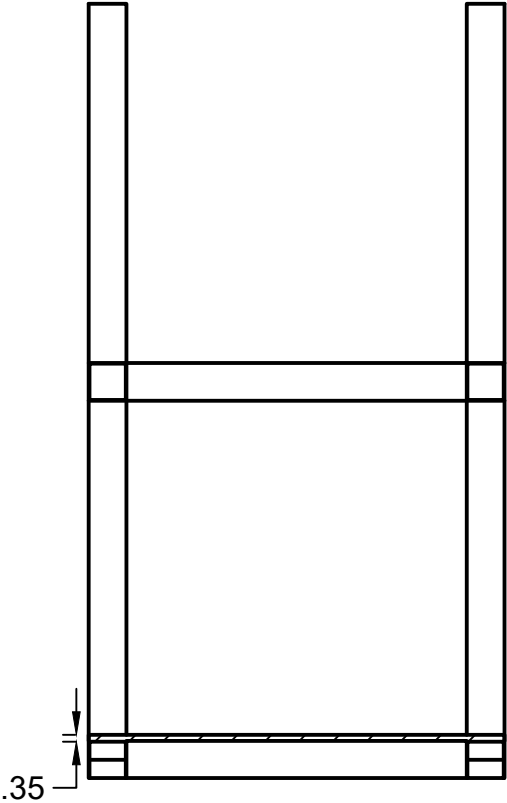
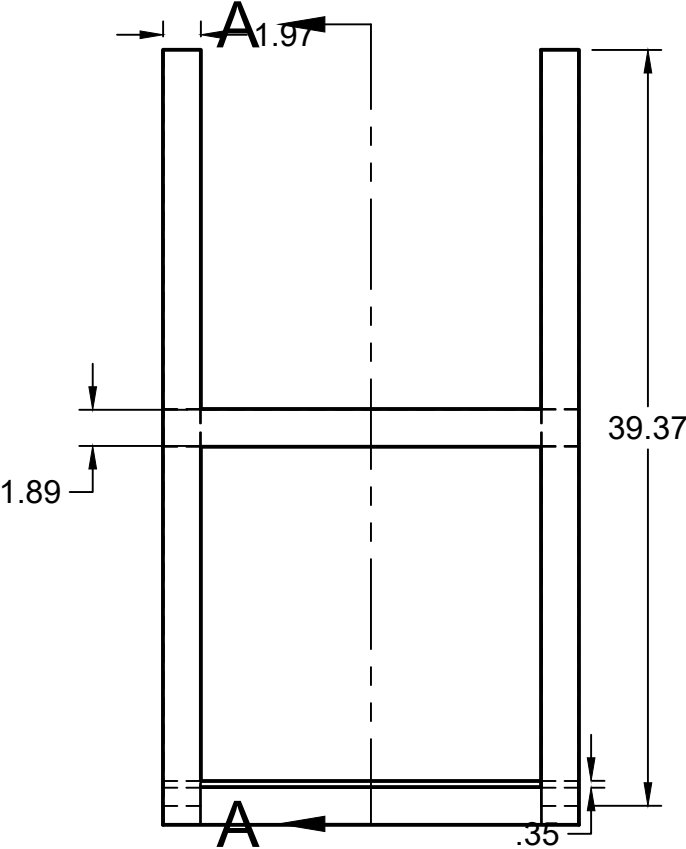
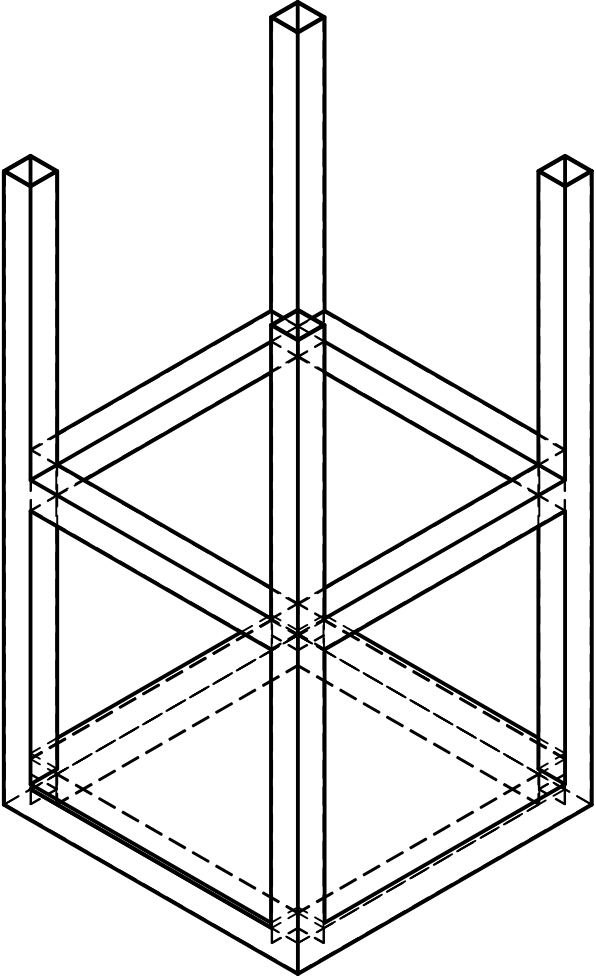


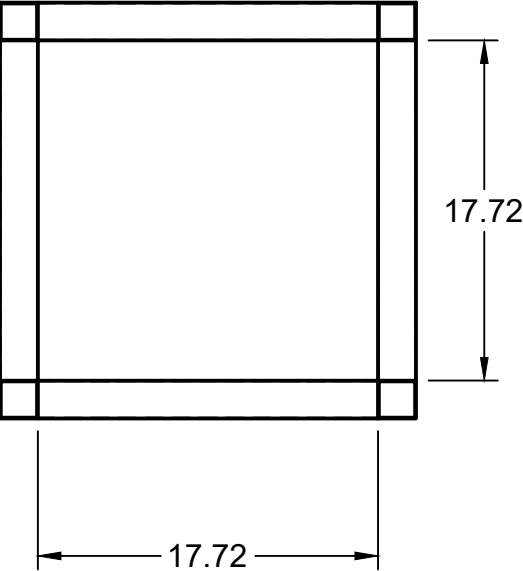

SECTION A-A
SCALE 1:10

		PROJECT Admin Project			
		TITLE stand			
APPROVED		SIZE	CODE	DWG NO	REV
CHECKED		B			
DRAWN	supreeth bs 21-05-2026	SCALE 1:10 (From parent)		WEIGHT	SHEET 1/1